



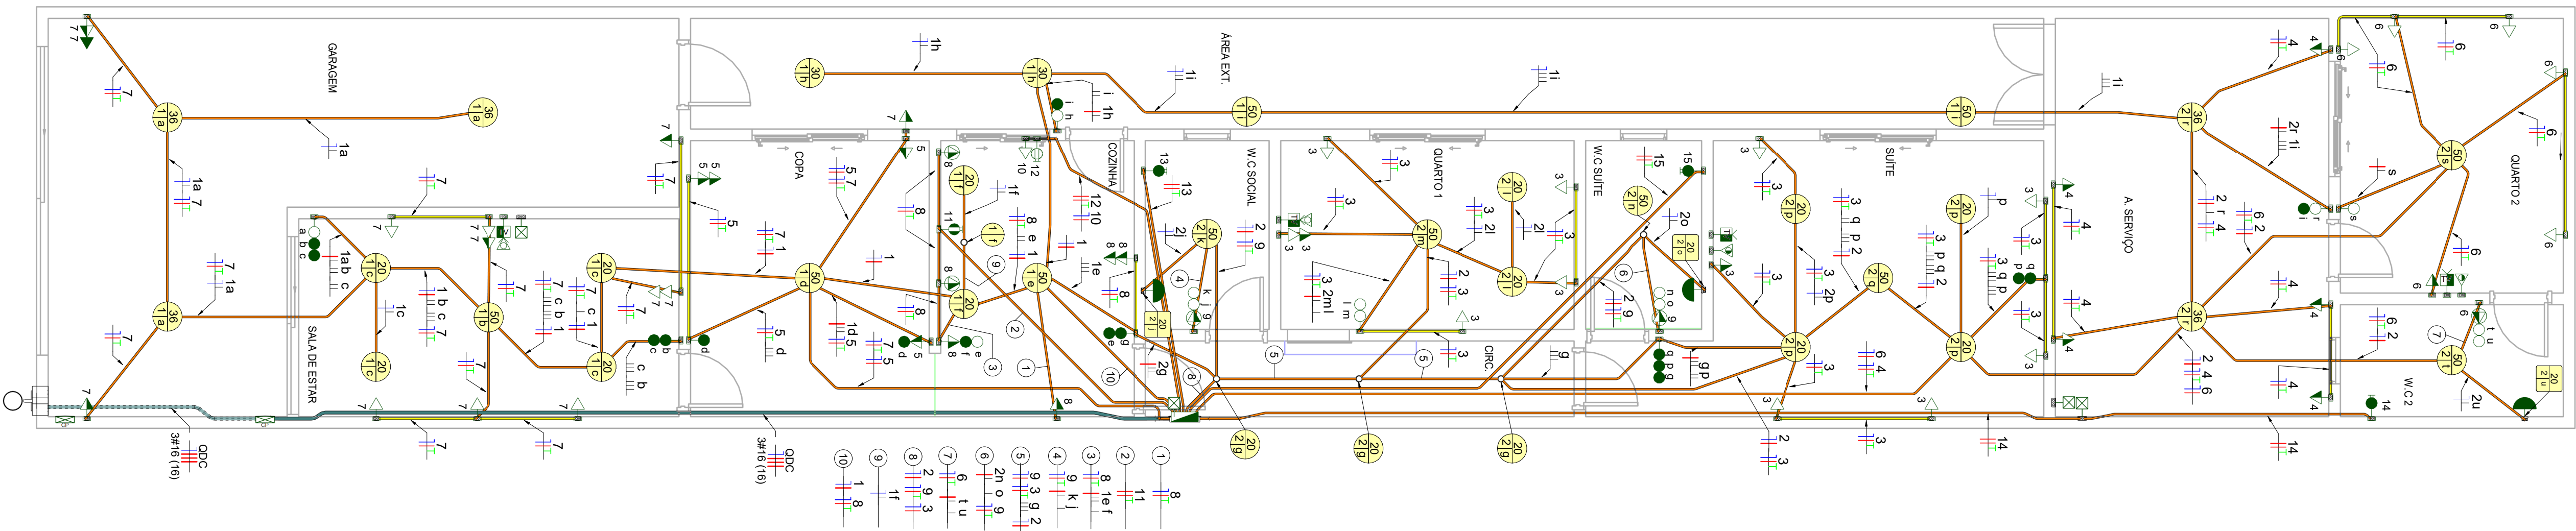

1
1 : 50
Térreo Fiação

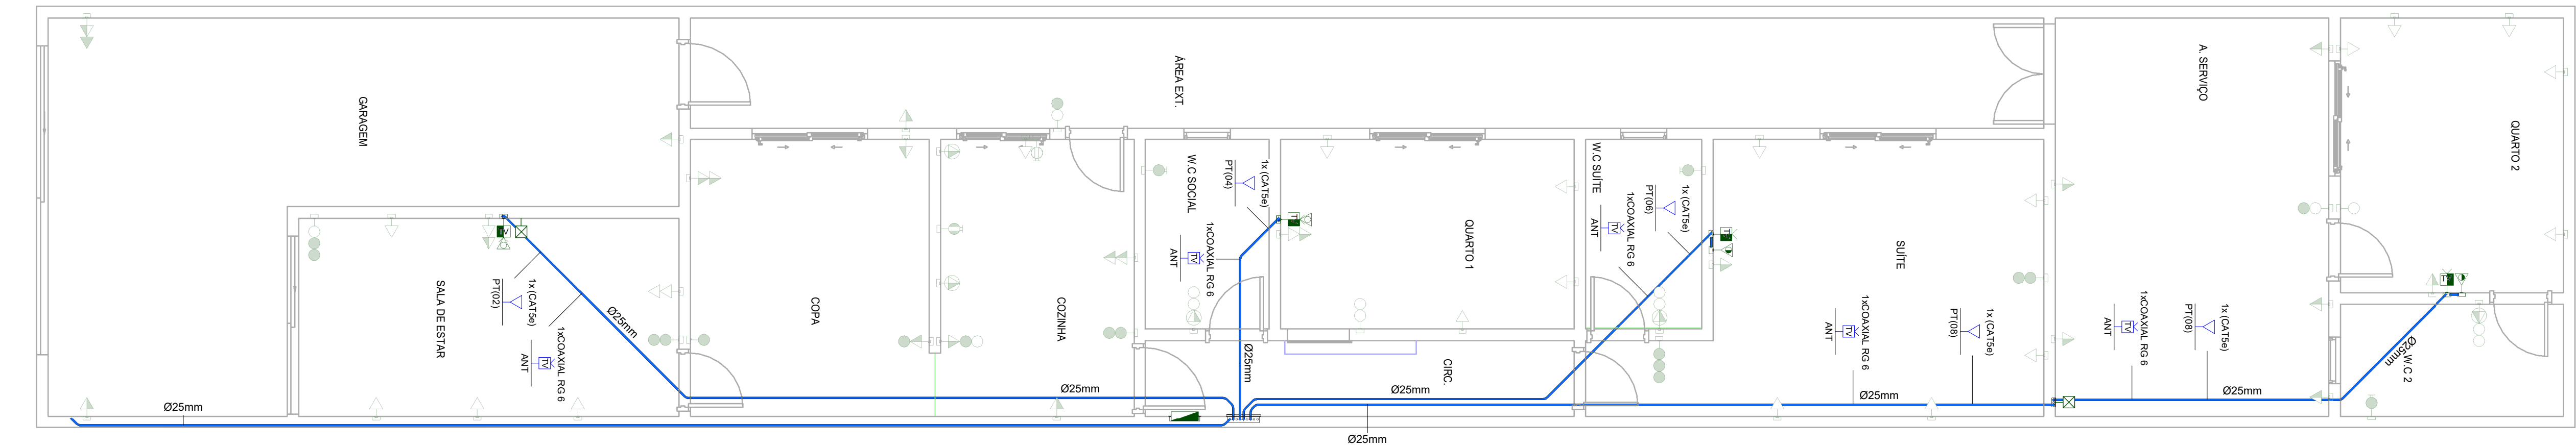

3
1 - 50
Térreo VDI

SIMBOLOGIA REDE, TELEFONIA E ANTENA

SIMBOLOGIA REDE, TELEFONIA E ANTENA	
	Ponto de Telefone, RJ11, a 0,30 m do piso, embutido em caixa 4x2
	Ponto de Telefone, RJ11, a 1,10 m do piso, embutido em caixa 4x2
	Ponto de Rede, RJ45, a 0,30 m do piso, embutido em caixa 4x2
	Ponto de Rede, RJ45, a 1,10 m do piso, embutido em caixa 4x2
	Ponto de Telefone, RJ45, altura indicada, embutido em caixa 4x2
	Ponto de TV, n° do ponto, a 0,30 m do piso, embutido em caixa 4x2
	Ponto de TV, n° do ponto, a 1,10 m do piso, embutido em caixa 4x2
	Ponto de TV, n° do ponto, a 2,10 m do piso, embutido em caixa 4x2

LEGENDA DE ELETRODUTOS

LEGENDA ELETRODUTOS	
	Eletroduto Rosçável
	Eletroduto Corrugado Amarelo
	Duto Azul TV, Dados e Telefone
	Eletroduto Corrugado Reforçado Laranja
	Eletroduto PEAD
	Cabo Bipolar
	Cabo Tripolar
	Eletroduto Rosçável embutido no piso
	Eletroduto Corrugado Amarelo embutido no piso
	Duto Azul TV, Dados e Telefone embutido no piso
	Eletroduto Corrugado Reforçado Laranja embutido no piso
	Eletroduto PEAD embutido no piso
	Cabo Bipolar embutido no piso
	Cabo Tripolar embutido no piso

SIMBOLOGIA ELÉTRICA

SIMBOLOGIA ELÉTRICA	
	Tomada Baixa 2P+T, 10A, a 0,30 m do piso, embutido em caixa 4x2
	Tomada Média 2P+T, 10A, a 1,10 m do piso, embutido em caixa 4x2
	Tomada Alta 2P+T, 10A, a 2,10 m do piso, embutido em caixa 4x2
	Tomada Baixa 2P+T, 20A, a 0,30 m do piso, embutido em caixa 4x2
	Tomada Média 2P+T, 20A, a 1,10 m do piso, embutido em caixa 4x2
	Tomada Alta 2P+T, 20A, a 2,10 m do piso, embutido em caixa 4x2
	Tomada de Piso 2P+T, 10A
	Tomada de Teto 2P+T, 10A
	Módulo de tomada USB
	Ponto de Força com placa saída de fio, a 220cm do piso acabado
	Ponto de Força com placa saída de fio, a "x" cm do piso acabado
	Interruptor simples de uma seção, embutido em caixa 4x2
	Interruptor paralelo, embutido em caixa 4x2
	Interruptor intermediário, embutido em caixa 4x2
	Pulsador
	Ponto para campainha
	Dimer (Variador de Luminosidade)
	Sensor de presença, embutido em caixa 4x2
	Ponto de luz embutido no teto
	Ponto de luz na parede a 210cm do piso acabado
	Eletroduto corrugado flexível embutido no teto ou na parede
	Eletroduto de PEAD embutido no piso
	Quadro geral de luz e força embutido a 1,50 do piso acabado
	Caixa para medidor
	Caixa de passagem no piso
	Caixa de passagem de passagem CPT de embutir na parede
	Caixa de passagem de passagem 4X2 ou 4x4" de embutir na parede
	Eletroduto que sobe
	Eletroduto que desce
	Eletroduto que passa descendo
	Eletroduto que passa subindo
	Condutores: Neutro, Fase, Terra e Retorno, respectivamente

NOTAS DE PROJETO

- OS CIRCUITOS QUE ALIMENTAM ÁREAS MOLHADAS OU SUJEITAS A LAVAGENS E CIRCUITOS QUE ALIMENTAM PONTOS DE UTILIZAÇÃO SITUADOS EM ÁREAS EXTERNAS À EDIFICAÇÃO DEVERÃO SER PROTEGIDOS POR DISPOSITIVOS DIFERENCIAIS RESIDUAIS DE 30mA EM CIRCUITOS INDIVIDUAIS OU AGUPADOS CONFORME INDICADO NO DIAGRAMA UNIFILAR DO PROJETO.
- OS CIRCUITOS PROTEGIDOS POR UM MESMO DISPOSITIVO DIFERENCIAL RESIDUAL DEVERÃO TER BARRAMENTO DE NEUTRO EXCLUSIVO E INDEPENDENTE, INTERLIGADO SOMENTE AOS SEUS ELEMENTOS PERTENCENTES.
- OS CIRCUITOS DEVERÃO SER PROTEGIDOS POR DISJUNTORES DE FABRICAÇÃO STECK OU SIMILAR TERMOMAGNÉTICOS SEGUINDO A NORMA ABNT NBR IEC 60898-2:2019, CURVA DE DISPARO TIPO "B" PARA CIRCUITOS RESISTIVOS E CURVA "C" PARA OS DEMAIS CIRCUITOS, CONFORME ESPECIFICADO NO DIAGRAMA UNIFILAR E QUADRO DE CARGAS.
- OS CABOS UTILIZADOS PARA CIRCUITOS TERMINAIS, SALVO ESPECIFICAÇÕES CONTRÁRIAS, DEVERÃO SER DE FABRICAÇÃO COBRECUM OU SIMILAR, FLEXÍVEIS, ENCORDAMENTO CLASSE 5, PVC 70° C - 750V.
- OS CABOS ALIMENTADORES DOS CENTROS DE DISTRIBUIÇÃO DEVERÃO SER DE FABRICAÇÃO COBRECUM OU SIMILAR, ISOLAÇÃO PVC 70° C - 450/750V - ENCORDAMENTO CLASSE 5.
- A COR DOS CONDUTORES DE NEUTRO DEVERÁ SER AZUL E DOS CONDUTORES DE PROTEÇÃO DEVERÁ SER VERDE E AMARELO, AS CORES DOS CONDUTORES DE FASE DEVERÃO SER VERMELHA PARA FASE A, CINZA PARA FASE B E BRANCO PARA FASE C.
- TODOS OS CIRCUITOS DEVERÃO POSSUIR CONDUTOR DE PROTEÇÃO EM TODA A SUA EXTENSÃO.
- O CONDUTOR DE NEUTRO NÃO PODERÁ SER UTILIZADO COMO CONDUTOR DE ATERRAMENTO, E O ATERRAMENTO FUNCIONAL DO PADRÃO DA CONCESSIONÁRIA NÃO PODERÁ SER CONSIDERADO COMO ATERRAMENTO DE PROTEÇÃO DA EDIFICAÇÃO.
- AS EMENDAS NOS CONDUTORES DEVERÃO OCORRER ÚNICA E EXCLUSIVAMENTE DENTRO DAS CAIXAS DE PASSAGEM E NUNCA DENTRO DE ELETRODUTOS E QUADROS DE DISTRIBUIÇÃO.
- AS EMENDAS NOS CONDUTORES COM SEÇÃO IGUAL OU INFERIOR A 4,0MM² DEVERÃO SER PROTEGIDAS POR FITA ISOLANTE DE FABRICAÇÃO 3M SCOTCH 33+ OU CONECTORES DE TORÇÃO.
- AS EMENDAS EM CONDUTORES COM SEÇÃO SUPERIOR A 4,0MM² DEVERÃO SER FEITAS COM O USO DE CONECTORES TIPO "PARAFUSO FENDIDO" DE COBRE E PROTEGIDAS POR FITA ISOLANTE DE AUTOFUSÃO SCOTCH (MR) 23BR.
- OS CONDUTORES DOS SISTEMAS DE REDE DE TELEFONIA, ANTENA, LÓGICA, SOM, ETC DEVERÃO PASSAR EM ELETRODUTOS EXCLUSIVOS E INDEPENDENTES DA REDE ELÉTRICA.
- ELETRODUTOS EMBUTIDOS EM LAJES, ALVENARIAS E CONTRAPIÇOS INTERNOS, PODERÃO SER SUBSTITUÍDOS POR FLEXÍVEIS OU CORRUGADOS, REFORÇADOS 750N/5CM (LARANJA) CONFORME NBR 15465.
- OS TUBOS EMBUTIDOS NAS LAJES NÃO DEVERÃO SER INSTALADOS DENTRO DAS NERVURAS ESTRUTURAIS, MAS SIM EM CAVIDADES ABERTAS NO EPS DA LAJE.
- AS EXTREMIDADES DAS TUBULAÇÕES EM PVC RÍGIDO NAS CAIXAS DE PASSAGEM DE PISO E CENTROS DE DISTRIBUIÇÃO DEVERÃO TER ACABAMENTO COM BUCHAS E ARRUELAS.
- AS SEÇÕES DE COMANDO DOS INTERRUPTORES ESTÃO INDICADAS EM PLANTA POR LETRAS ALFABÉTICAS.
- AS TOMADAS COM POTÊNCIAS NÃO INDICADAS SERÃO CONSIDERADAS DE 100W.
- FIACÃO SEM INDICAÇÃO SERÃO CONSIDERADAS DE 2,5MM².
- ELETRODUTOS NÃO INDICADOS TERÃO DIÂMETRO NOMINAL DE 25mm (3/4").
- OS QUADROS DE DISTRIBUIÇÃO DEVERÃO SER INSTALADOS A 1,50M DO PISO ACABADO.
- OS QUADROS DE DISTRIBUIÇÃO E MEDIÇÃO DEVERÃO SER ATERRADOS CONFORME PRESCRITO NA NBR 5410:2004.
- OS QUADROS DE DISTRIBUIÇÃO SERÃO PROVIDOS DE PORTAS COM FECHADURA, CONTRA-TAMPA FIXADA MECANICAMENTE ATRAVÉS DE PORCAS E PARAFUSOS, POSSUIR BARRAMENTO TRIFÁSICO TIPO PINO OU PENTE, BORNES PARA NEUTRO E TERRA E TRILHOS PARA DISJUNTORES NORMA DIN (IEC/NEMA) E AUXILIARES PARA DISPOSITIVOS DR DE FABRICAÇÃO CEMAR, PIAL OU SCHNEIDER.
- TENSÃO SECUNDÁRIA DE SERVIÇO 380/220V - 60HZ FORNECIMENTO EM BAIXA TENSÃO.
- PARA UTILIZAÇÃO DE CARGAS SUPERIORES ÀS NÃO PREVISTAS E QUE INFLUENCIEM NA DEMANDA DA EDIFICAÇÃO, O PROJETISTA DEVERÁ SER COMUNICADO PREVIAMENTE

BROK

SOLUÇÕES ELÉTRICAS

PROJETO	CONTEÚDO DA FOLHA	
Projeto Elétrico	Planta de Fiação, Planta VDI e Detalhe interno do QDC	
ENDEREÇO DA OBRA	ÁREA	
	180m²	
AUTOR DO PROJETO	FASE DO PROJETO	
Designer	Projeto Executivo	
RESP. TÉCNICO	NOME DA FOLHA	
	Planta de Fiação e Planta VDI	
EMIÇÃO INICIAL	ESCALA	ÚLTIMA REVISÃO
20/10/2026	1:50	
ARQUIVO	FOLHA	REVISÃO
ELE-SP145	02	RV-01